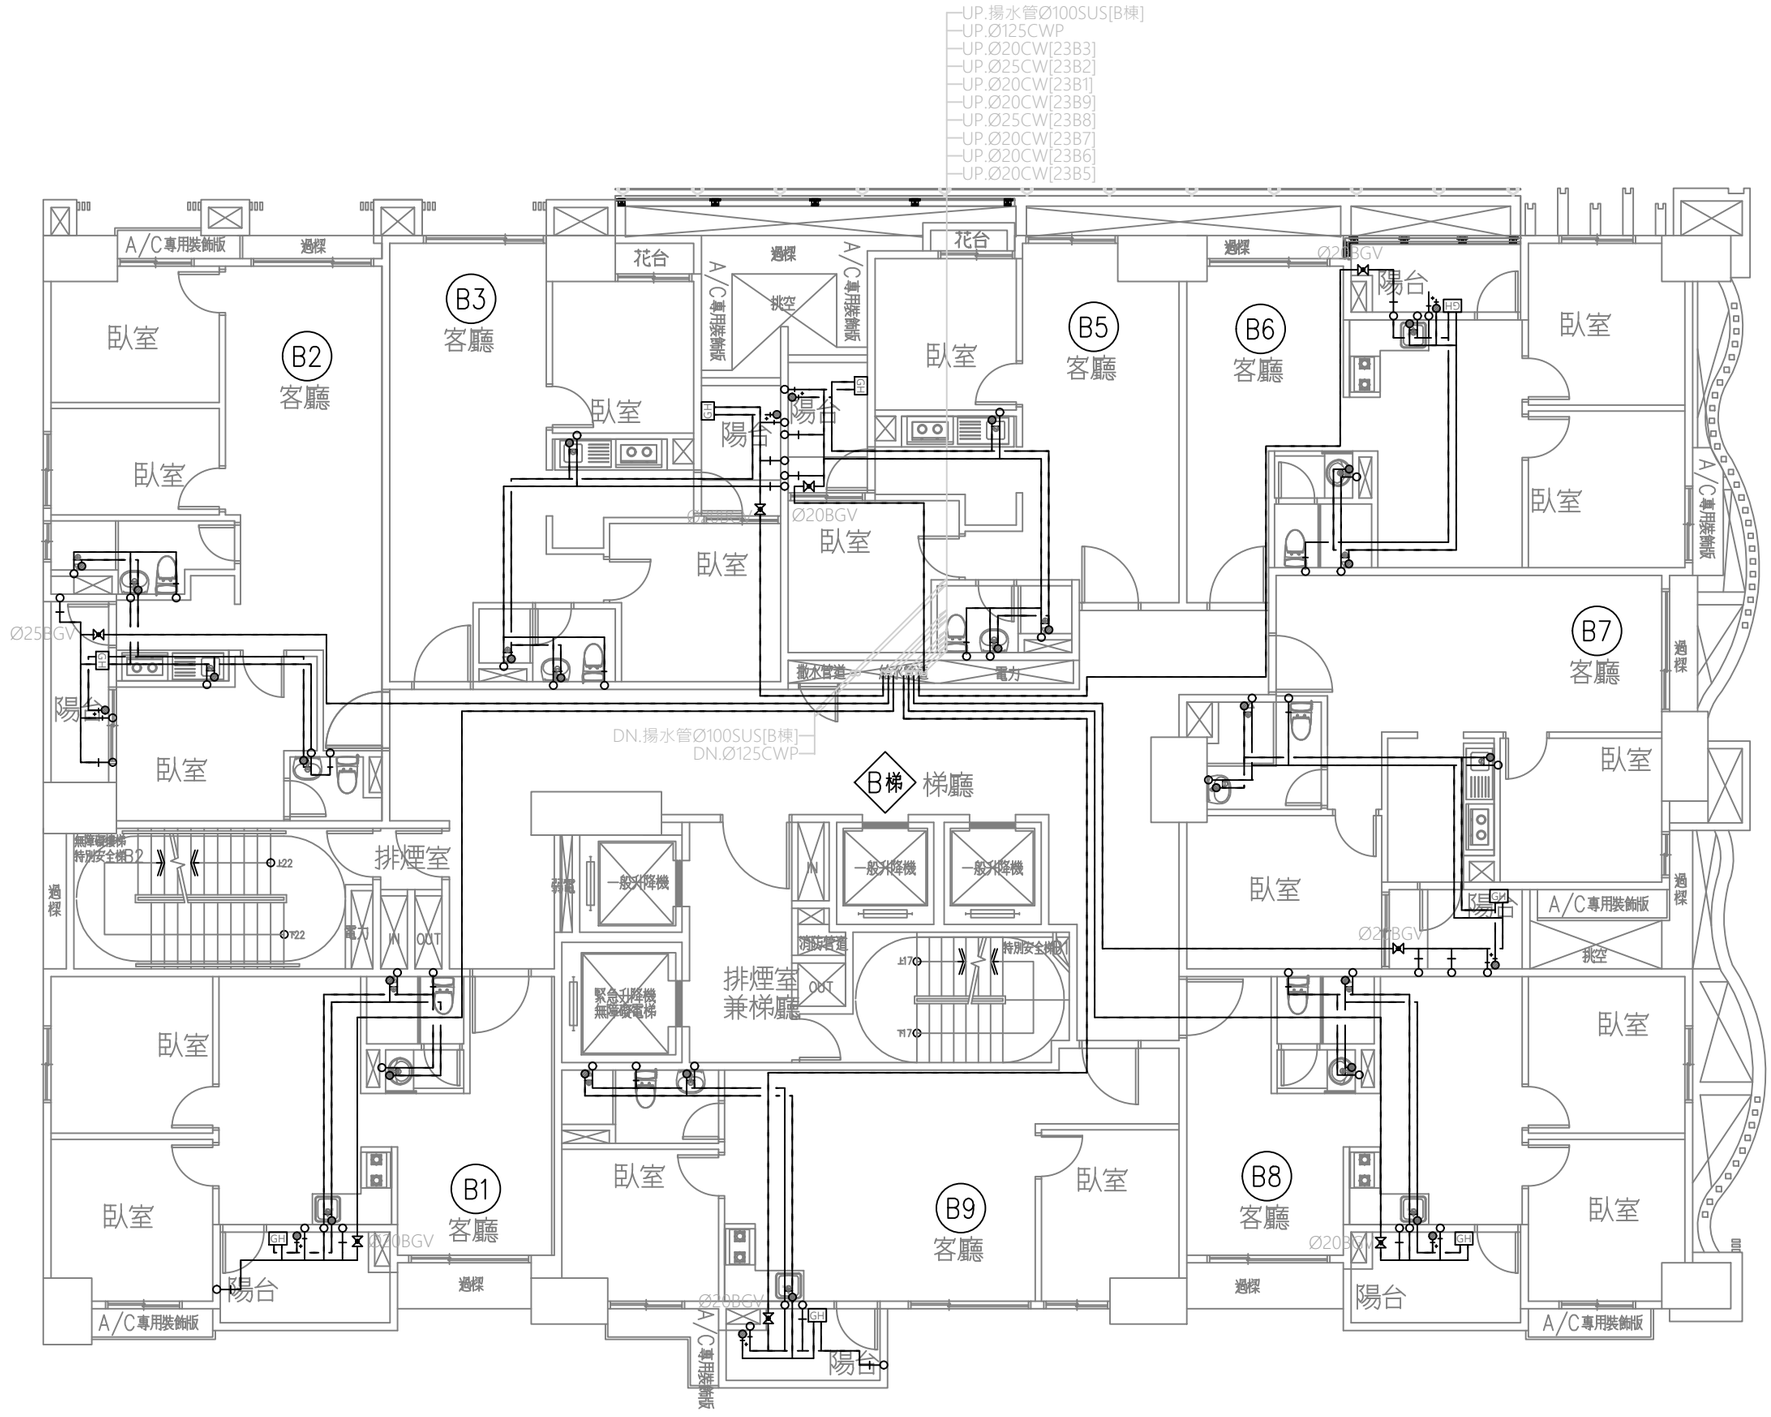


B棟－23F　給水配置圖

君邑建築
捷堡營造工程有限公司
地址:新北市林口區文化二路一段398號16樓
電話:(02)22010888　傳真:(02)22795999

工程名稱
PROJECT
君邑羅浮

圖檔名稱
FILE NAME

圖面名稱
DRAWING TITLE

NO.	日期 DATE	內容 CONTENTS
1.		
2.		
3.		
4.		
5.		
6.		

繪圖 DRAWN BY
設計 DESIGNED BY
建築師 ARCHITECT
覆核 REAPPROVED BY
比例 SCALE
單位 UNIT
日期 DATE
圖號 SHEET NO.
圖號 DRAWING NO.