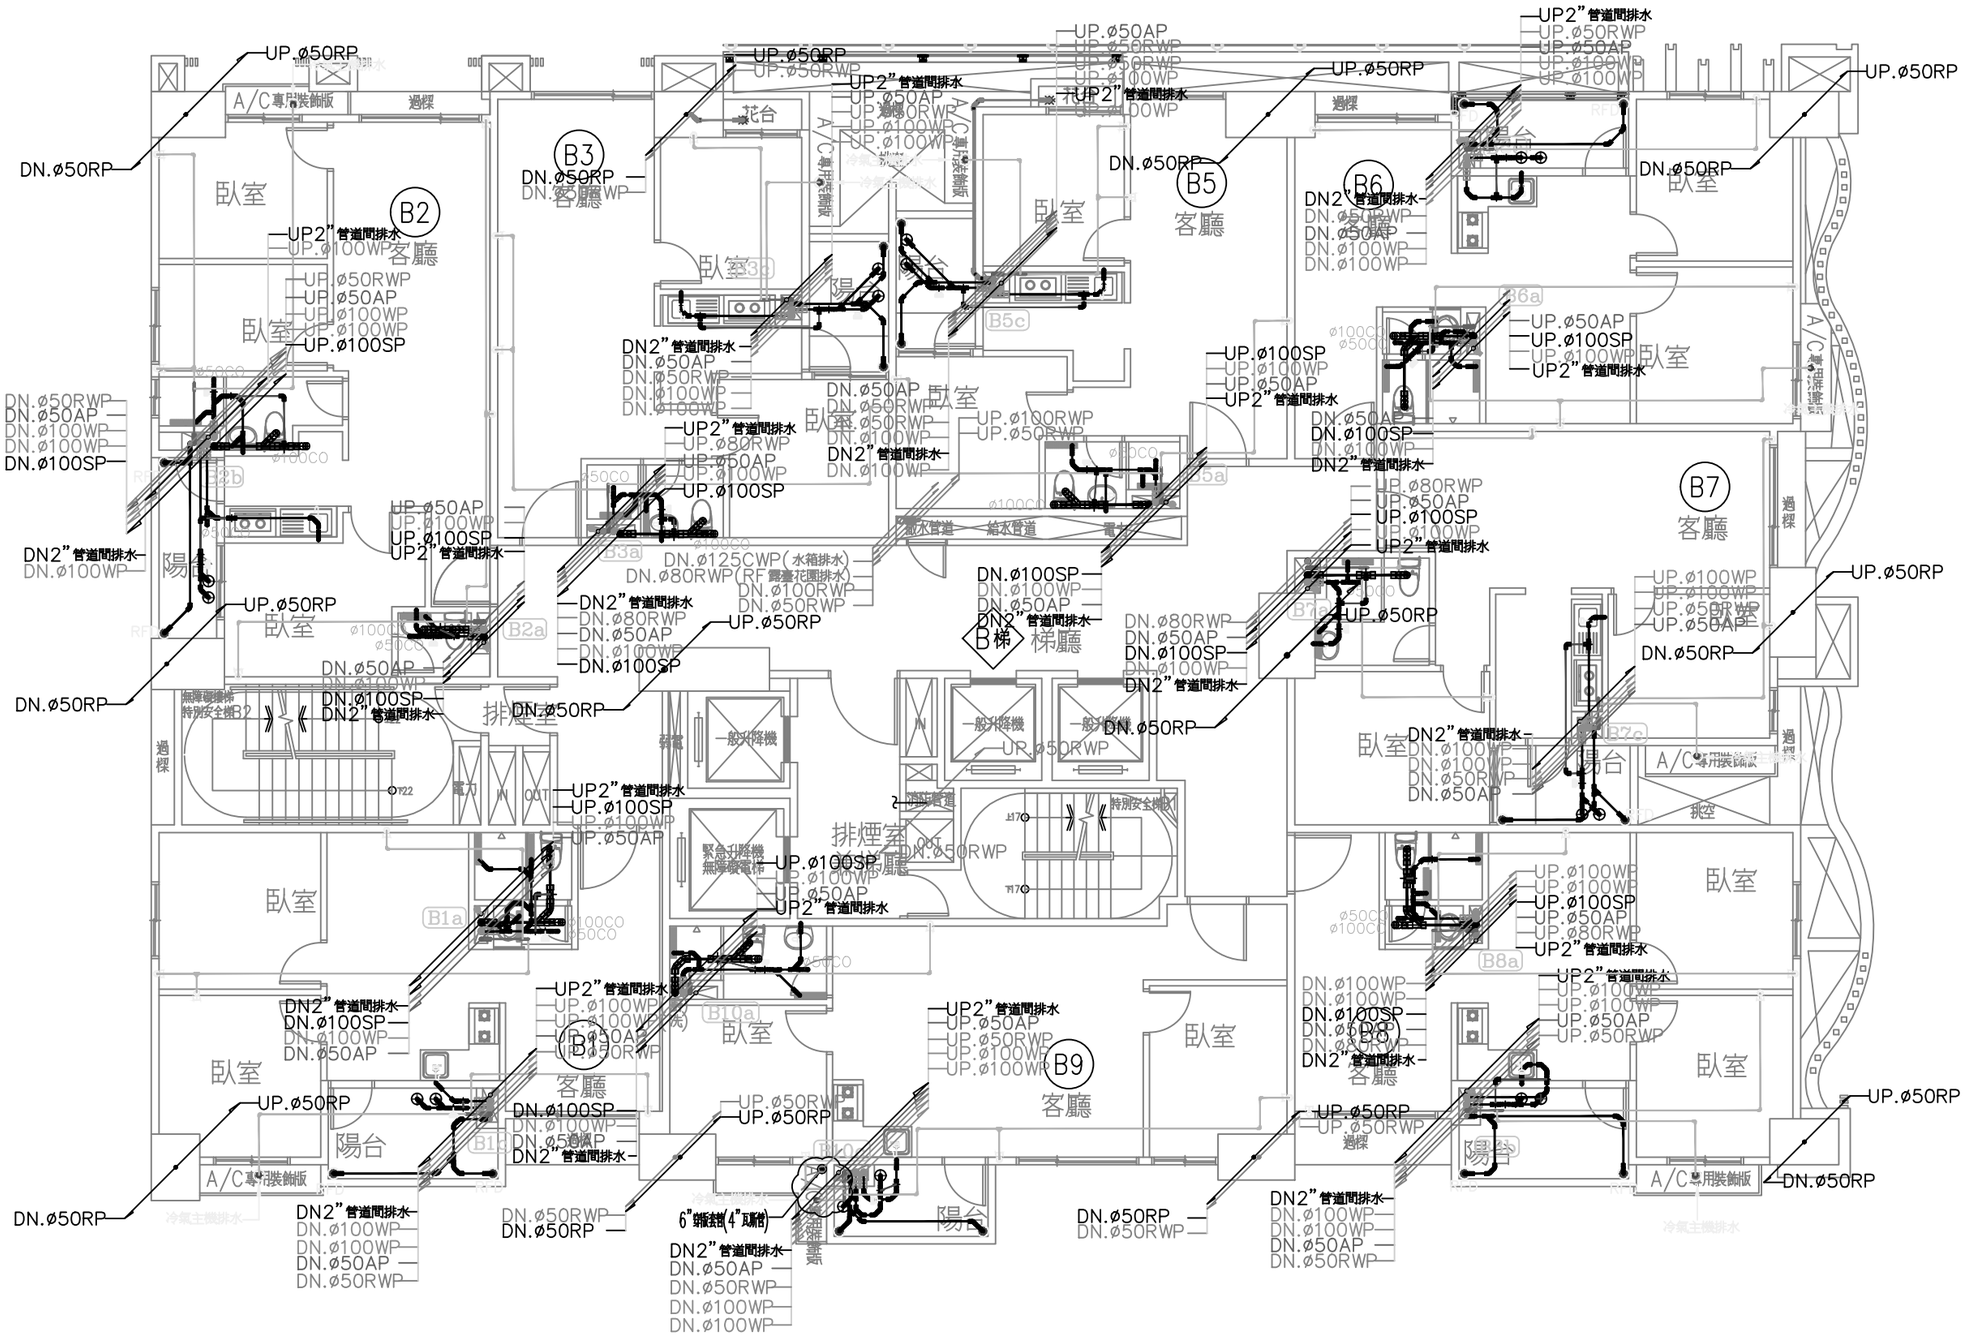



# B棟－23F　排水配置圖


君邑建築
捷堡營造工程有限公司
地址:新北市林口區文化二路一段399號16樓
電話:(02)22010888　傳真:(02)22795999


工程名稱
PROJECT
君邑羅浮

圖檔名稱
FILE NAME

圖面名稱
DRAWING TITLE

| NO. | 日期 DATE | 內容 CONTENTS |
|---|---|---|
| 1. | | |
| 2. | | |
| 3. | | |
| 4. | | |
| 5. | | |
| 6. | | |

繪圖 DRAWN BY
設計 DESIGNED BY
工務 ARCHITECT
覆核 REAPPROVED BY
比例 SCALE
單位 UNIT
日期 DATE
圖號 SHEET NO.